
MMUCO ORION DUPLEX – DRAFT 0.2

Option C2: M4(2) + Bathroom A – concept floor plan, two mirrored single-storey dwellings

Client-approved concept baseline 24 Oct 2026 – NOT FOR CONSTRUCTION – NOT A PLANNING OR BUILDING REGULATIONS COMPLIANCE DRAWING

PDF sheet: ISO A1 portrait at 1:50. Dimensions in mm. For any other print size use the scale bar; do not scale from prints.

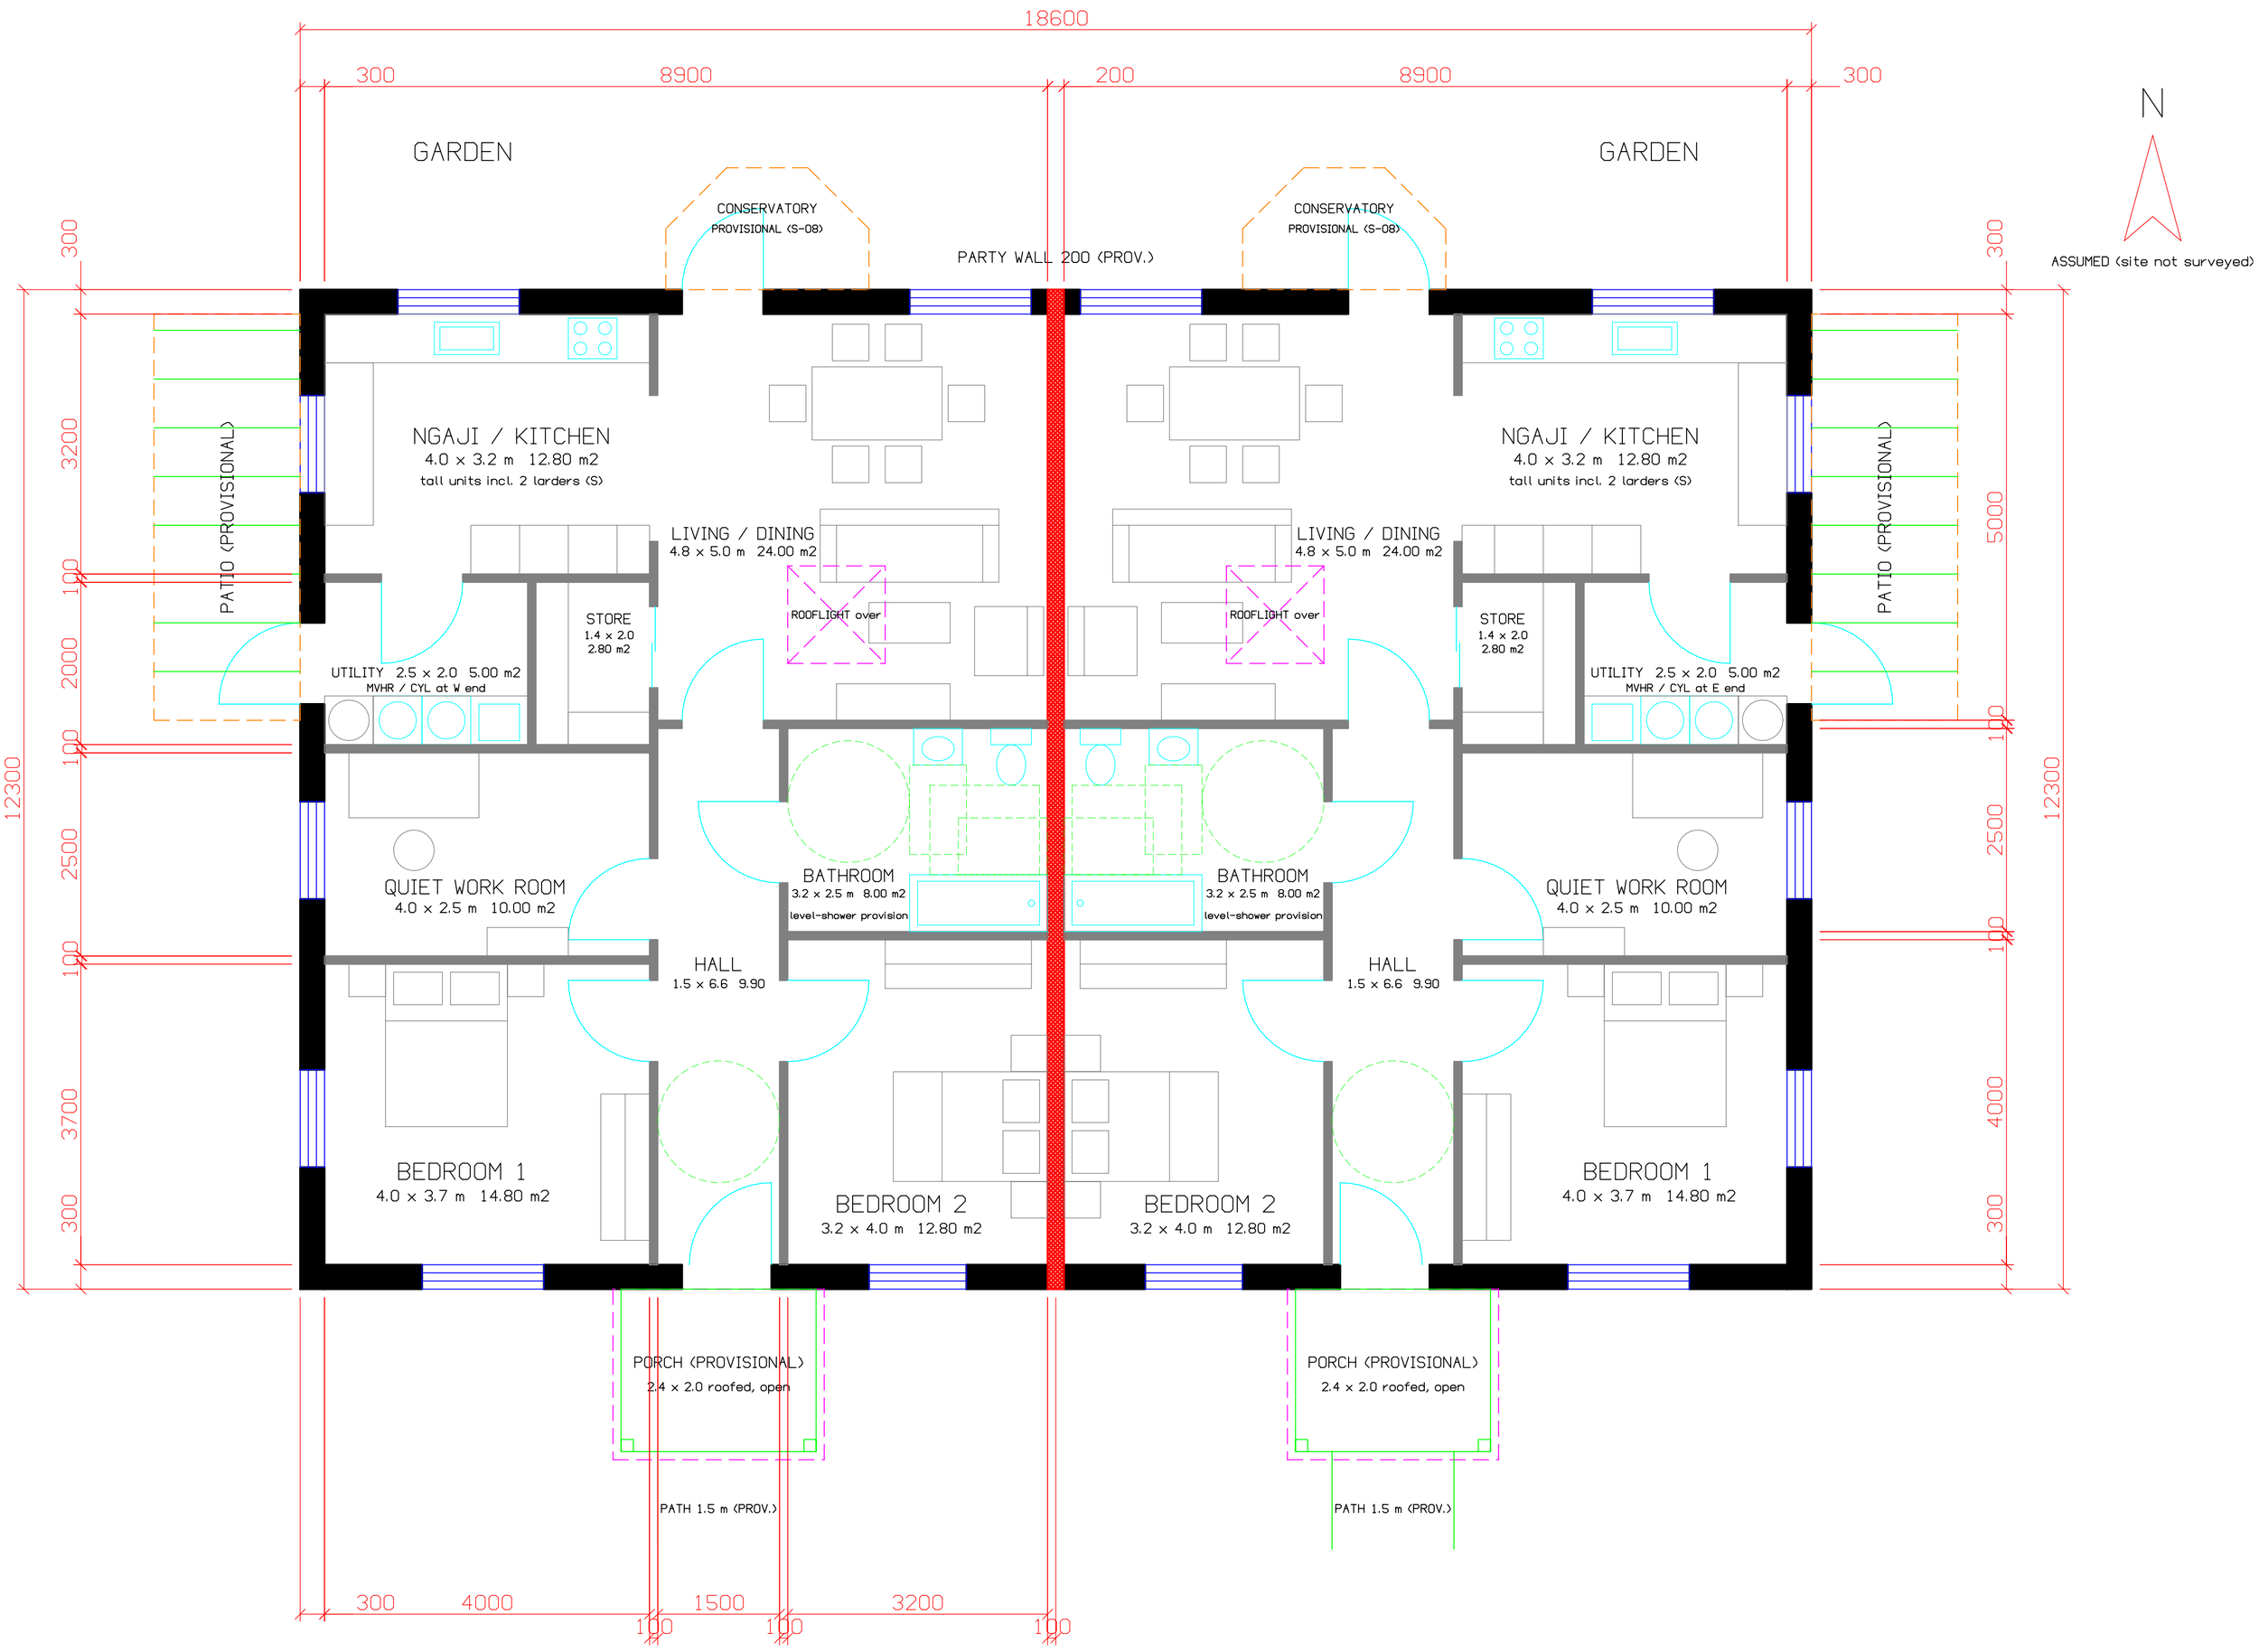

DWELLING A

DWELLING B (MIRRORED)

NOTES – DRAFT 0.2 (OPTION C2)

1. Units mm. Room sizes are CLEAR INTERNAL (finished face to finished face); overall dimensions are EXTERNAL. GIA per dwelling 104.13 m2 (NDSS para 8; internal faces of perimeter walls, incl. partitions). Building footprint 18.60 x 12.30 m = 228.78 m2. Dwelling B mirrors dwelling A about the party-wall centreline.
2. Accessibility target M4(2) – an optional requirement that applies only where a planning condition requires it (ADM Vol 1 para 0.3). Bathroom A: bath, WC and basin to ADM Diagram 2.5 with provision for a future level-access shower at the bath position; bathroom door opens outward (2.27d). Living-room principal window sill max 850 mm (2.24c). Conservatory door 1,000 opening (approx. 850 clear).
3. Ventilation: MVHR (ADF 2021 paras 1.67–1.73). Unit allowance in utility/plant; duct routes TBD (roof not designed). Purge ventilation by openable windows and the rooflight.
4. Rooflight over living/dining approx. 1.0 m2 net glazing, openable, solar-control glazing and external blind. Size and position subject to daylight (BS EN 17037) and overheating (ADO / TM59) assessment.
5. Food storage: tall larder units in the kitchen (no walk-in pantry).
6. PROVISIONAL (not yet supported by evidence): wall build-ups 300/200/100; orientation (north assumed); conservatory size (S-08 2.5 x 1.5 m); porches, patios, 1.5 m paths and all external works. Site boundary NOT SHOWN (no survey). Battery storage location NOT SHOWN.
7. Concept drawing only. Geometry tested by script; NOT a planning, Building Regulations (Parts B, E, F, K, L, M, O) or fire-safety compliance claim. Professional review required.
8. Draft 0.1 is retained unchanged (MMUCO_ORION_Duplex_Floor_Plan.dxf).

ROOM SCHEDULE (per dwelling, clear internal)

Bedroom 1: 4.00 x 3.70 m = 14.80 m2
Bedroom 2: 3.20 x 4.00 m = 12.80 m2
Quiet work room: 4.00 x 2.50 m = 10.00 m2
Living / dining: 4.80 x 5.00 m = 24.00 m2
Ngaji / kitchen: 4.00 x 3.20 m = 12.80 m2
Bathroom (A): 3.20 x 2.50 m = 8.00 m2
Utility and plant: 2.50 x 2.00 m = 5.00 m2
Store: 1.40 x 2.00 m = 2.80 m2
Hall: 1.50 x 6.60 m = 9.90 m2
NIFA 100.10 + partitions 4.03 = GIA 104.13 m2
Two dwellings: GIA 208.26 m2; footprint 228.78 m2

DIMENSION KEY

EXTERNAL: overall dimensions (18600, 12300) and the chains outside the building, set out from outer wall faces through wall and partition faces.
CLEAR INTERNAL: room sizes in the room labels and the room schedule (finished face to finished face).
PROVISIONAL: every wall-thickness segment (300 external, 200 party, 100 partition) and therefore the overall dimensions; porch 2.4 x 2.0, patio 1.8 x 5.0, conservatory 2.5 x 1.5 and path 1.5 m (labelled, not dimensioned).

LEGEND

- External wall 300 (build-up provisional)
- Party (separating) wall 200 (provisional)
- Internal partition 100
- Roof elements above: rooflight, porch roof
- PROVISIONAL: conservatory, patio
- Accessibility reference zones (ADM M4(2))
- Porch, path (external works, provisional)

SCALE BAR (metres)

0 1 2 3 4 5 m